# 广西贺州三棵树年产50万吨涂料及配套建设项目

比例尺：1:1000

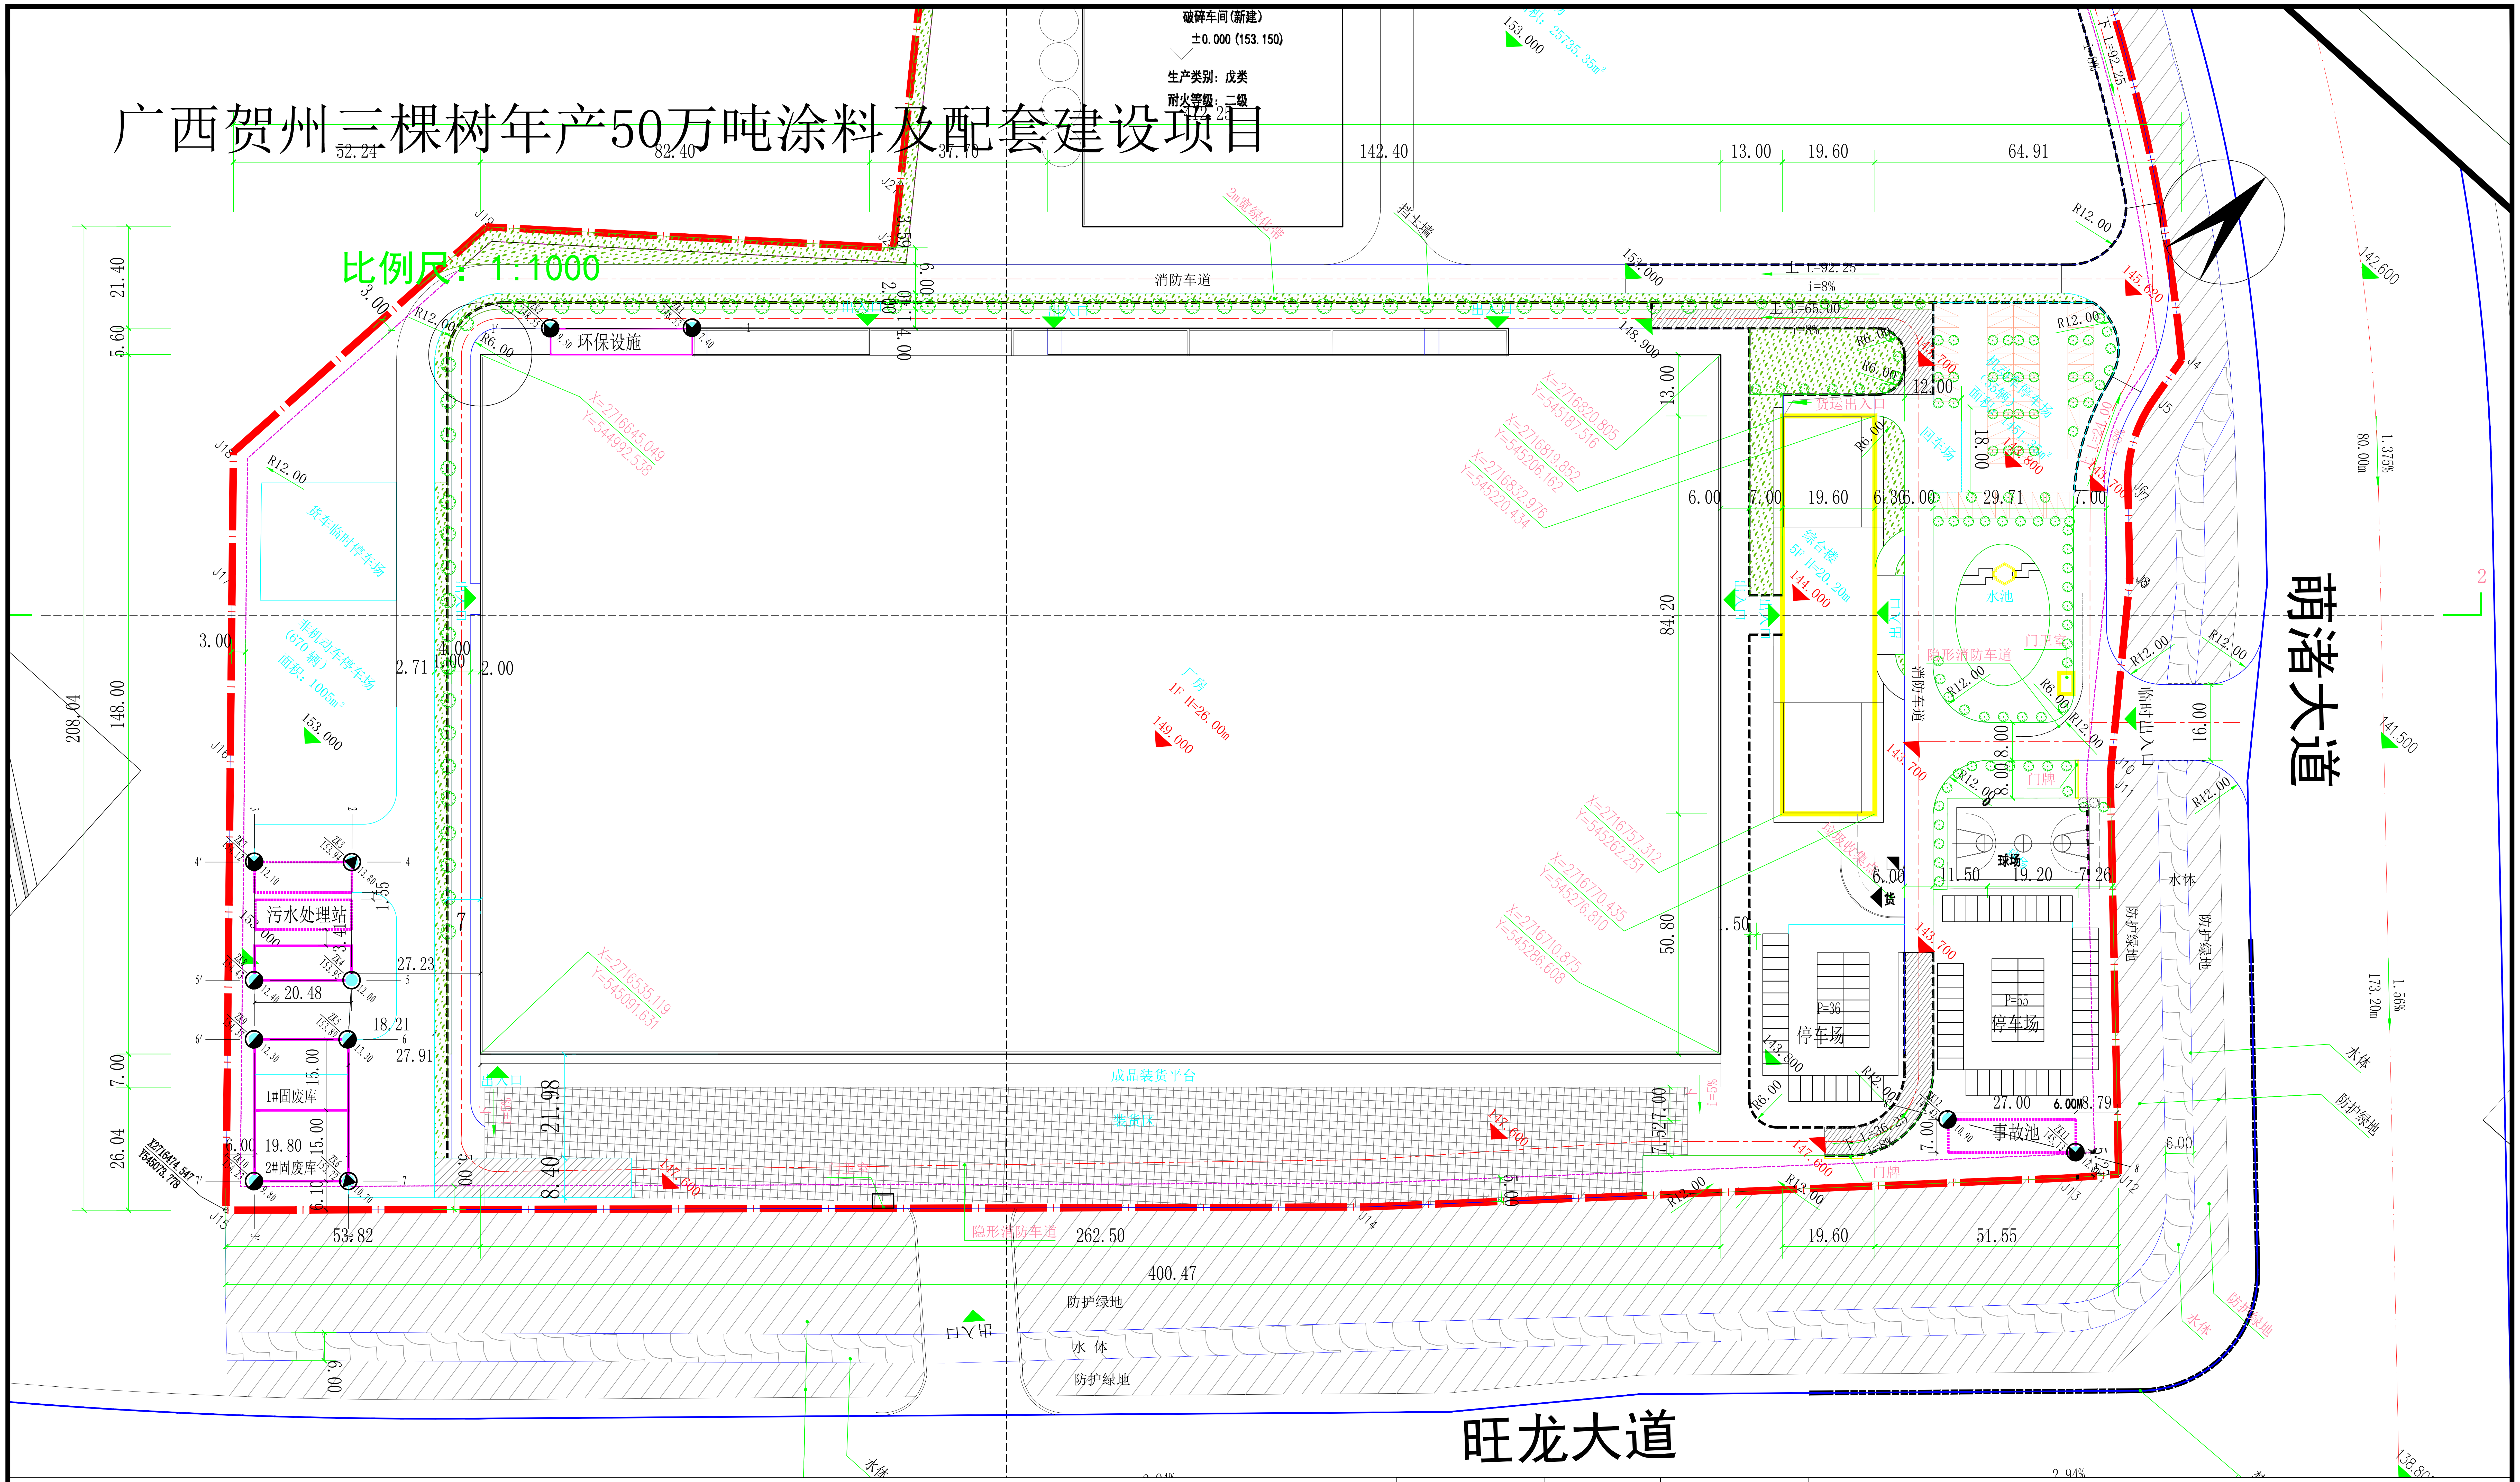

## 图 例

钻孔编号

○ 鉴别孔

拟建筑物及地上层数

已有建筑物

| | | | | | | | |
|---|---|---|---|---|---|---|---|
| 审　　定 | 阮成清 | | 广西昇龙工程勘察设计检测有限公司 | | | | |
| 审　　核 | 郑　义 | 郑义 | 资质等级：甲级　　证书编号：B245015689 | | | | |
| 项目负责 | 贺　瑞 | 贺瑞 | 建设单位 | 广西贺州市矿投智科碳酸钙开发有限公司 | | | |
| 校　　对 | 李可茂 | 李可茂 | 项目名称 | 广西贺州三棵树年产50万吨涂料及配套建设项目 | | | |
| 制　　图 | 颜　康 | 颜康 | 平面图 | 图号 | 1 | 日期 | 2026.5.10 |

Autodesk

# 广西贺州三棵树年产50万吨涂料及配套建设项目

比例尺：1:500

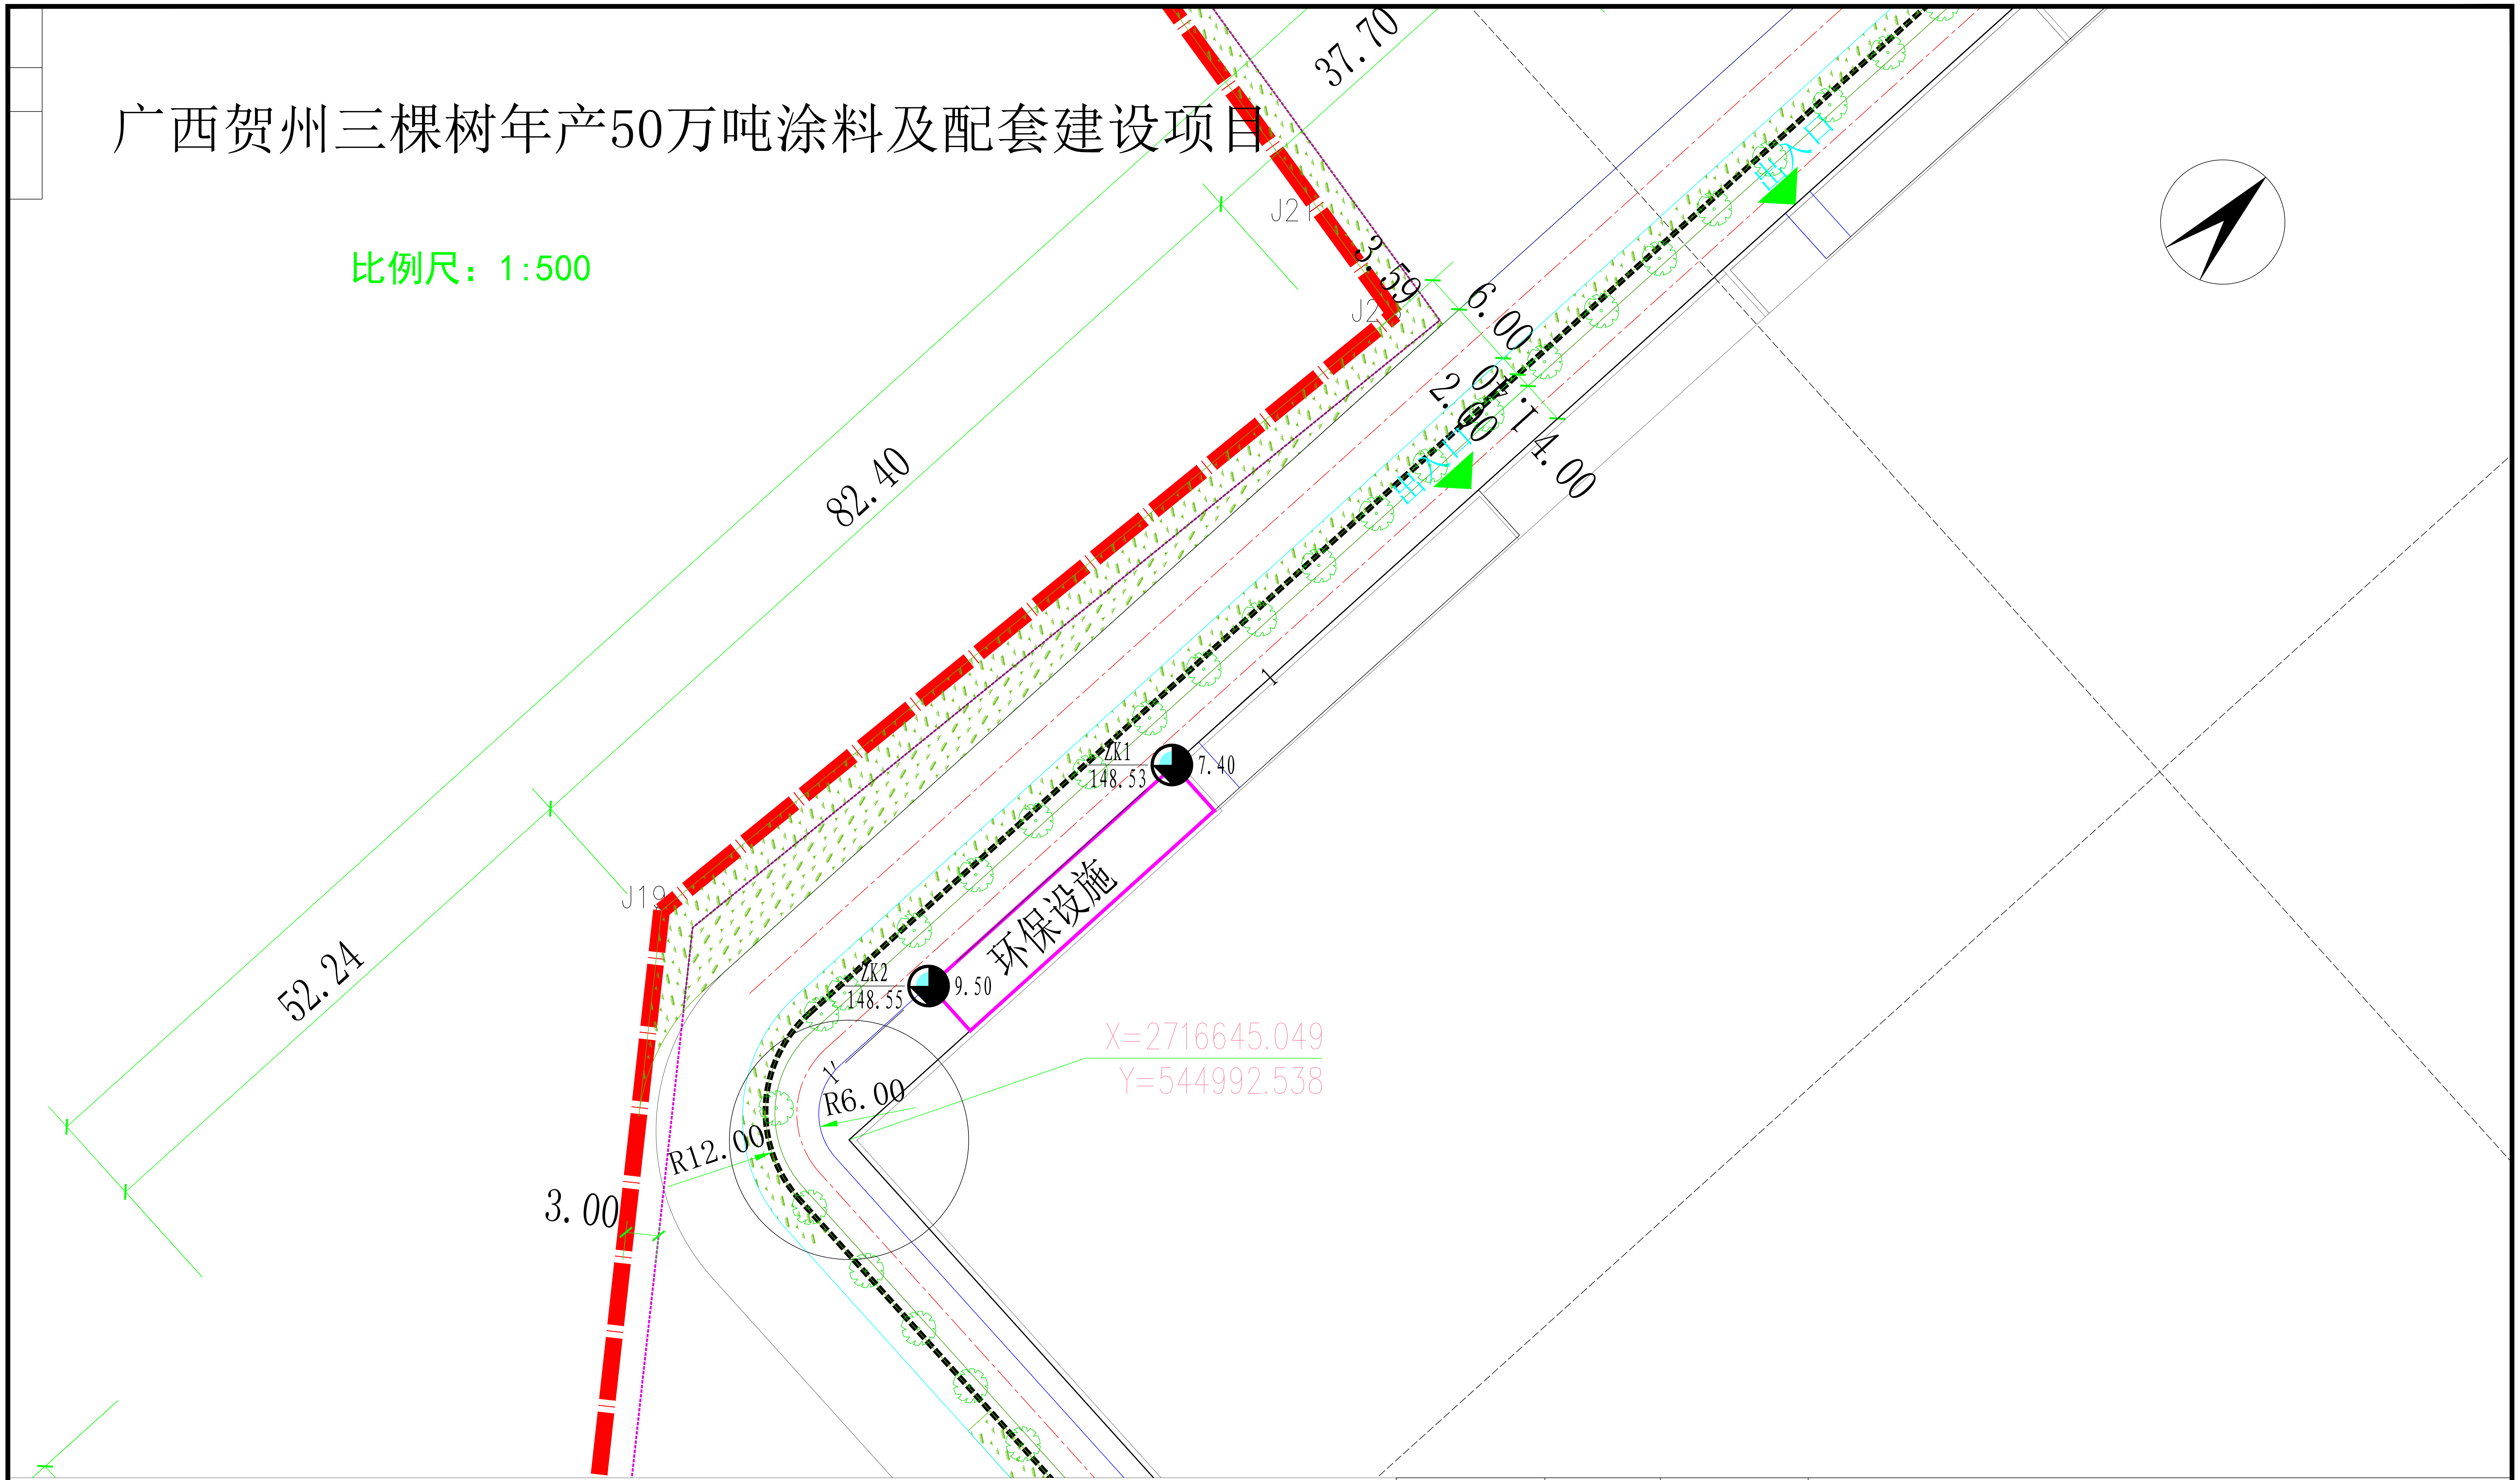

图例

钻孔编号 ○

○ 鉴别孔

拟建筑物及地上层数

已有建筑物

|  |  |  |  |  |  |  |  |
|---|---|---|---|---|---|---|---|
| 审定 | 阮成清 | 阮成清 | 广西昇龙工程勘察设计检测有限公司 |  |  |  |  |
| 审核 | 郑义 | 郑义 | 资质等级：甲级 证书编号：B245015689 |  |  |  |  |
| 项目负责 | 贺瑞 | 贺瑞 | 建设单位 | 广西贺州市矿投智科碳酸钙开发有限公司 |  |  |  |
| 校对 | 李可茂 | 李可茂 | 项目名称 | 广西贺州三棵树年产50万吨涂料及配套建设项目 |  |  |  |
| 制图 | 颜康 | 颜康 | 平面图 | 图号 | 2 | 日期 | 2026.5.10 |

# 广西贺州三棵树年产50万吨涂料及配套建设项目

比例尺：1:500

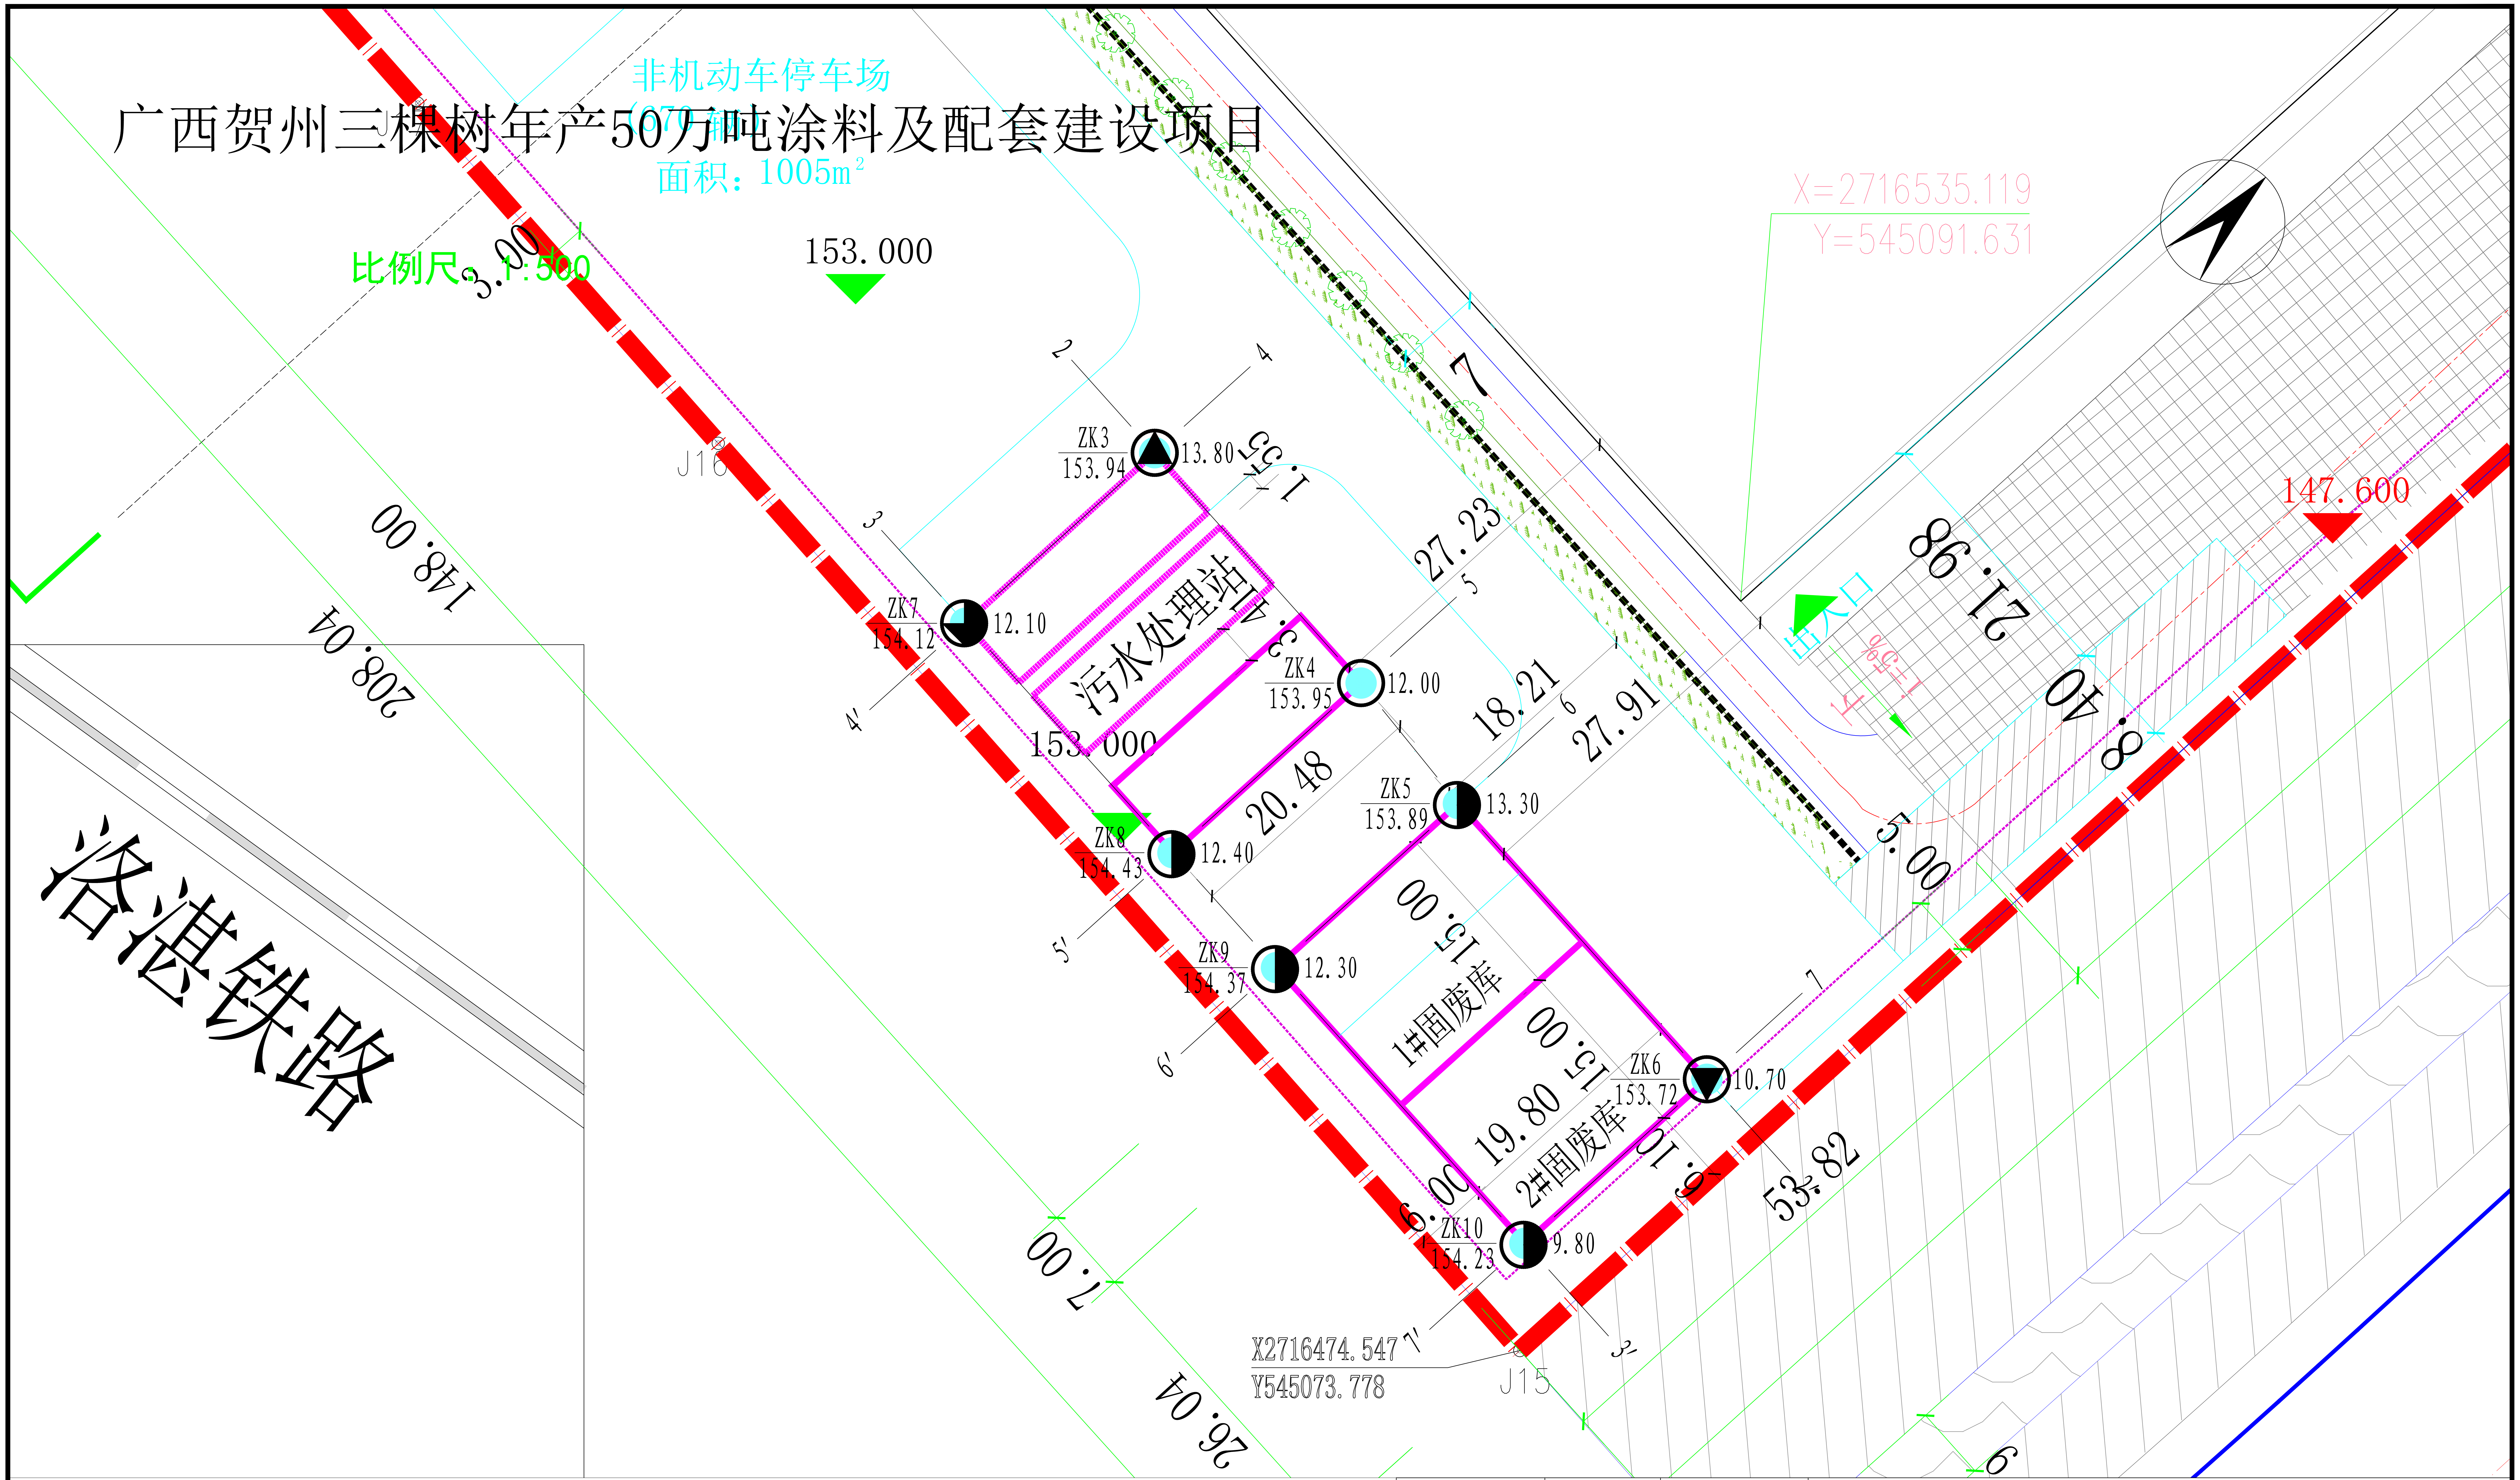

图 例

钻孔编号 ○

○ 鉴别孔

拟建筑物及地上层数

已有建筑物

| | | | | |
|---|---|---|---|---|
| 审　定 | 阮成清 | 阮成清 | 广西昇龙工程勘察设计检测有限公司 | |
| 审　核 | 郑　义 | 郑义 | 资质等级：甲级　证书编号：B245015689 | |
| 项目负责 | 贺　瑞 | 贺瑞 | 建设单位 | 广西贺州市矿投智科碳酸钙开发有限公司 |
| 校　对 | 李可茂 | 李可茂 | 项目名称 | 广西贺州三棵树年产50万吨涂料及配套建设项目 |
| 制　图 | 颜　康 | 颜康 | 平面图 | 图号 3　日期 2026.5.10 |

# 广西贺州三棵树年产50万吨涂料及配套建设项目

比例尺：1:600

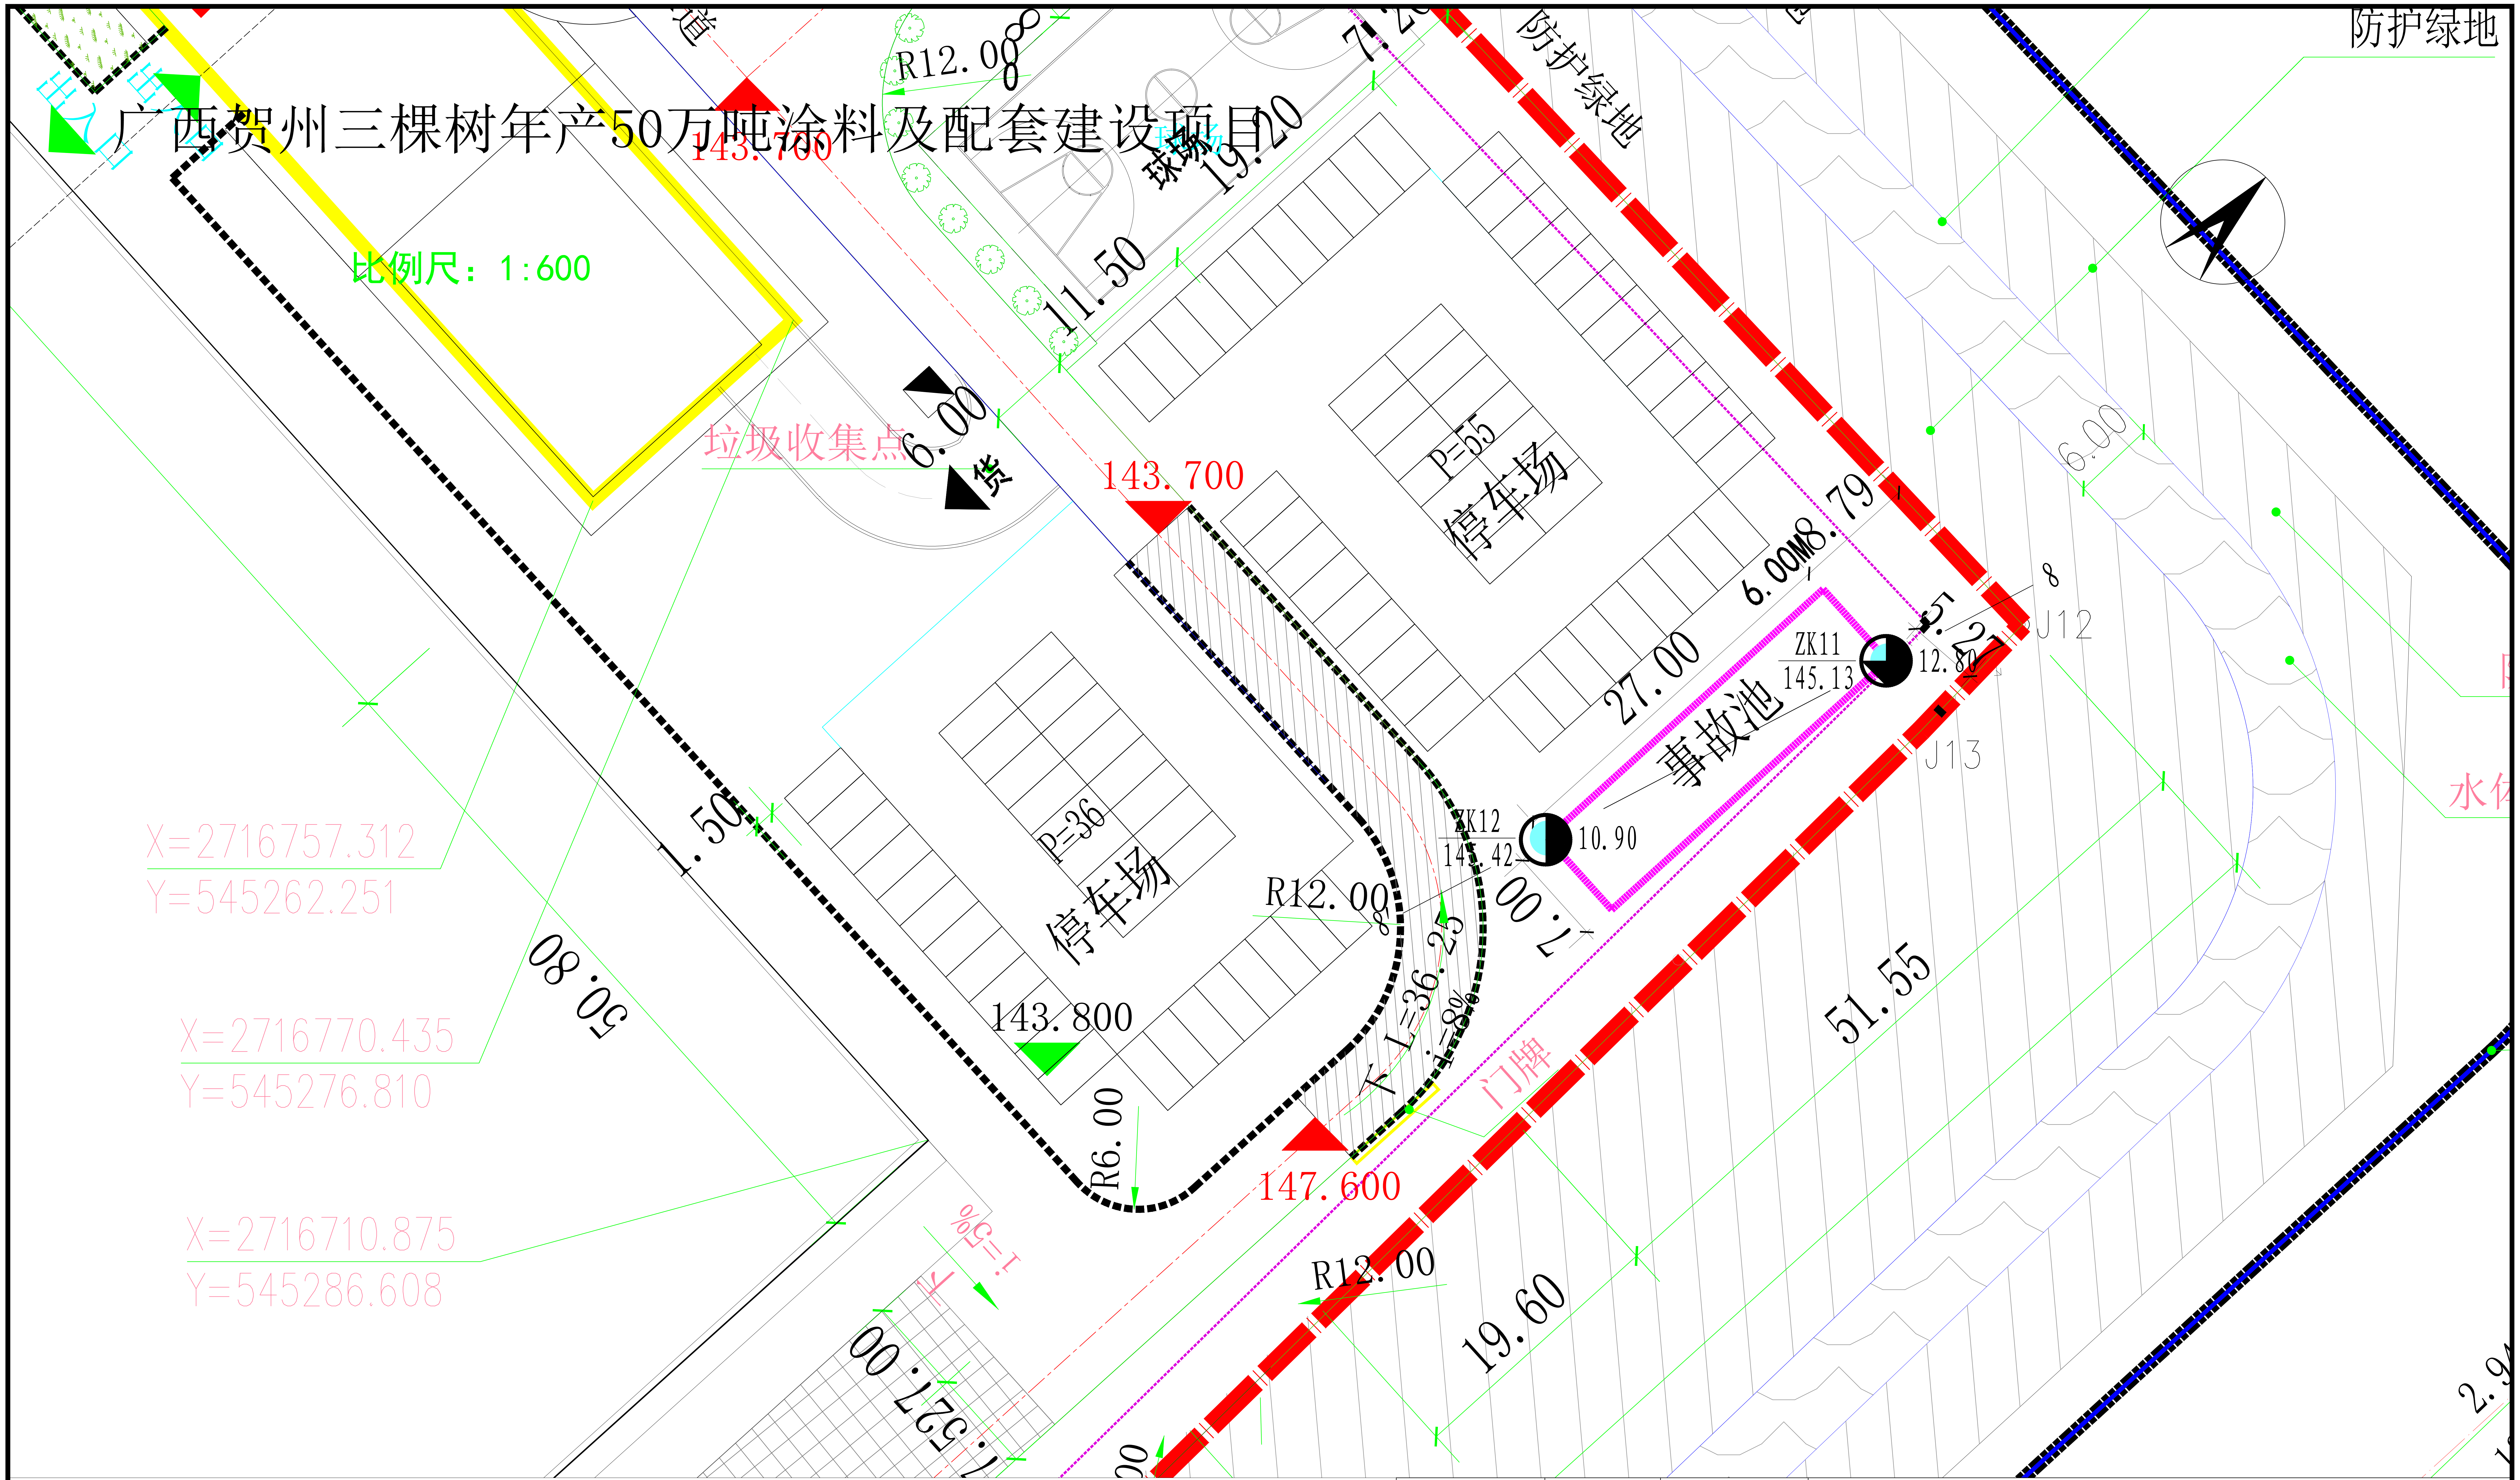

## 图 例

钻孔编号○

○ 鉴别孔

拟建筑物及地上层数

已有建筑物

| | | | | | | | |
|---|---|---|---|---|---|---|---|
| 审　定 | 阮成清 | 阮成清 | 广西昇龙工程勘察设计检测有限公司<br>资质等级：甲级　证书编号：B245015689 | | | | |
| 审　核 | 郑　义 | 郑义 | | | | | |
| 项目负责 | 贺　瑞 | 贺瑞 | 建设单位 | 广西贺州市矿投智科碳酸钙开发有限公司 | | | |
| 校　对 | 李可茂 | 李可茂 | 项目名称 | 广西贺州三棵树年产50万吨涂料及配套建设项目 | | | |
| 制　图 | 颜　康 | 颜康 | 平面图 | 图号 | 4 | 日期 | 2026.5.10 |