建筑物与勘探点平面位置图

--比例尺 1:500

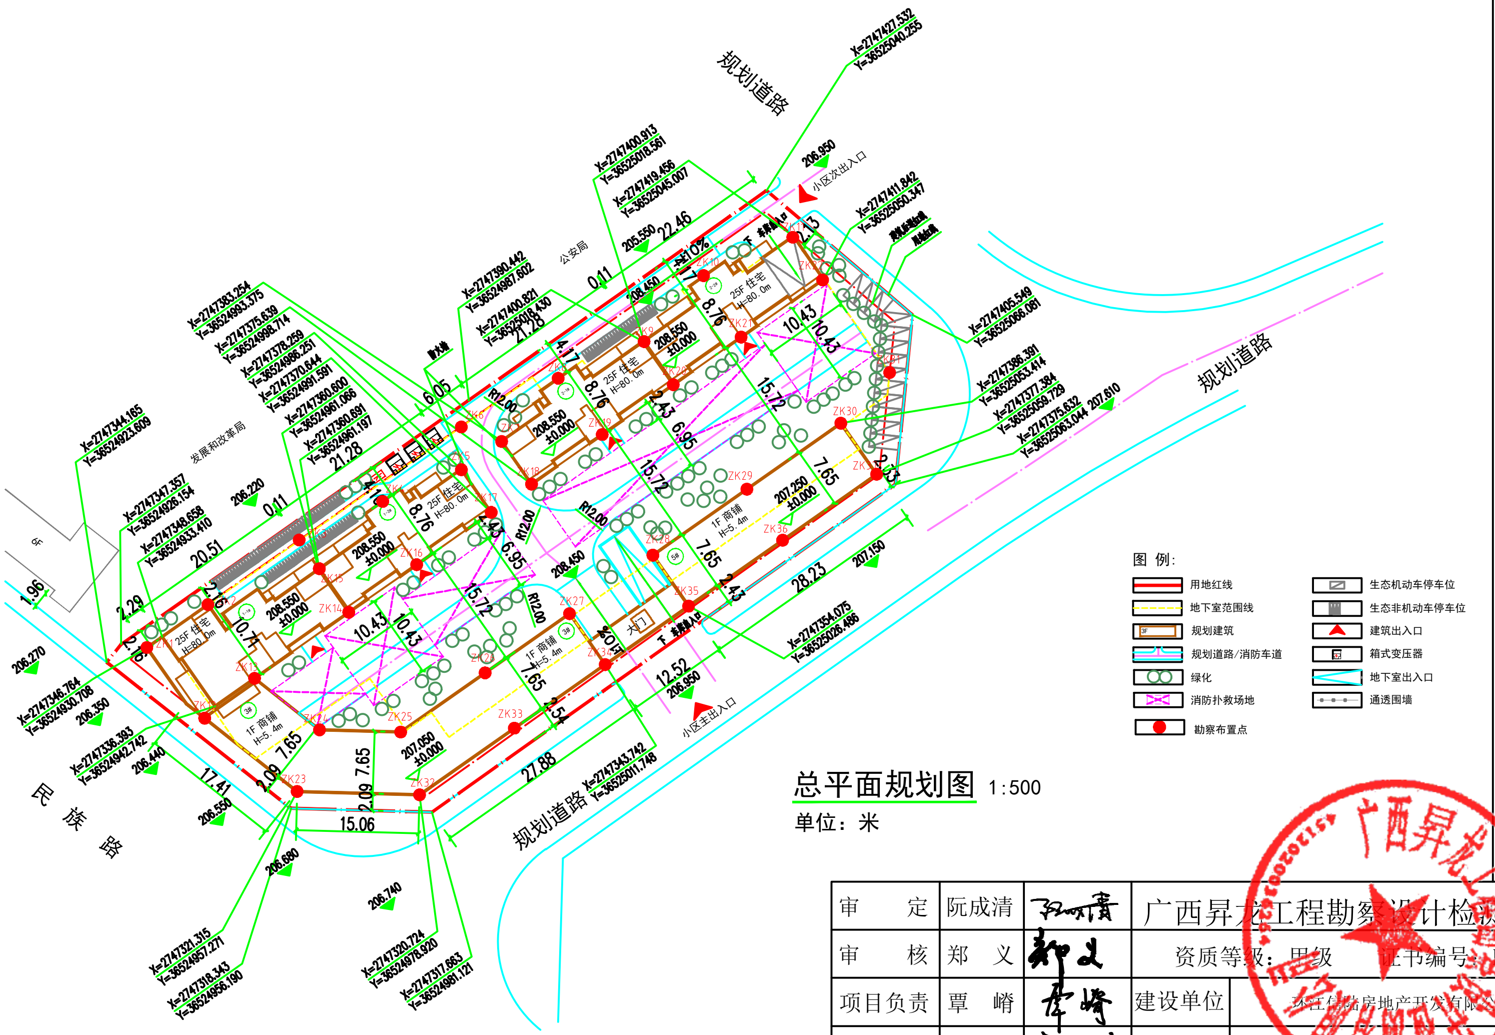
规划道路
规划道路
规划道路
民族路
小区次出入口
小区主出入口
公安局
发展和改革局
25F 住宅 H=80.0m
1F 商铺 H=5.4m
ZK1
ZK14
ZK23
ZK25
ZK27
ZK29
ZK30
ZK32
ZK33
ZK35
ZK36
208.550 ±0.000
207.250 ±0.000
207.050 ±0.000
206.950
206.220
206.270
206.350
206.440
206.550
206.680
206.740
207.150
207.610
205.550
208.450
X=2747427.532 Y=36525040.255
X=2747400.913 Y=36525018.561
X=2747419.456 Y=36525045.007
X=2747411.842 Y=36525050.347
X=2747405.549 Y=36525056.081
X=2747386.391 Y=36525053.414
X=2747377.384 Y=36525059.729
X=2747375.632 Y=36525063.044
X=2747354.075 Y=36525028.486
X=2747343.742 Y=36525011.748
X=2747390.442 Y=36524987.602
X=2747400.821 Y=36525018.430
X=2747383.254 Y=36524993.375
X=2747375.639 Y=36524998.714
X=2747344.165 Y=36524923.609
X=2747347.357 Y=36524926.154
X=2747348.658 Y=36524933.410
X=2747346.764 Y=36524930.708
X=2747336.393 Y=36524942.742
X=2747321.315 Y=36524957.271
X=2747318.343 Y=36524956.190
X=2747320.724 Y=36524978.920
X=2747317.663 Y=36524981.121
22.46
21.28
20.51
28.23
27.88
17.41
15.06
12.52
10.43
15.72
8.76
7.65
6.95
2.43
R12.00
图 例:
用地红线
地下室范围线
规划建筑
规划道路/消防车道
绿化
消防扑救场地
勘察布置点
生态机动车停车位
生态非机动车停车位
建筑出入口
箱式变压器
地下室出入口
通透围墙

总平面规划图 1:500

单位：米

审　　定	阮成清	阮成清	广西昇龙工程勘察设计检测有限公司				
审　　核	郑　义	郑义	资质等级：甲级　　证书编号：B245015689				
项目负责	覃　峭	覃峭	建设单位	环江信陆房地产开发有限公司			
校　　对	李可茂	李可茂	项目名称	阳光幸福里			
制　　图	莫家里	莫家里	平面图		图号	1	日期 2025.09